


Berm Construction Volume (cubic meters): 20538.76

Berm Holding Volume (cubic meters): 77776.69

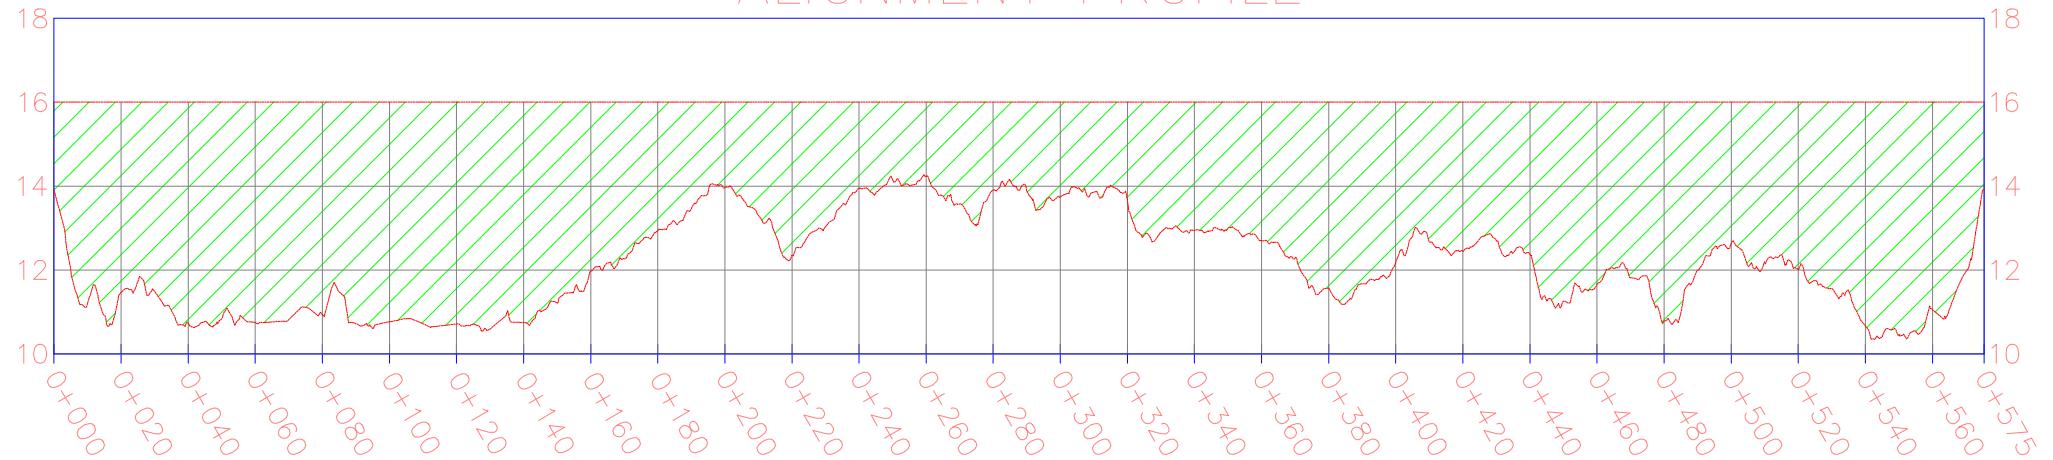

# ALIGNMENT PROFILE



		200 - 215 Cow Bay Road PRINCE RUPERT, B.C. V8J 1A2 PHONE: (250) 627-5899 FAX: (250) 627-5890
PROJECT: Ridley Island Export and Logistics Project		
DRAWING TITLE: Penguin Pond Overburden Storage Project		
PROJECT NUMBER:	DRAWING NUMBER:	SCALE: 1:2250
DATE: 25/08/05	CAD FILE: 2416	PAPER:
DRWNS: AC & CC	CHECKED: CG	DESCRIPTION: Penguin Pond Overburden Storage Project
DESIGN BY: APNS	DATE: 24/08/05	
Last Sheet: 5 of 7 Date: 5/7/2005 2:38 PM		