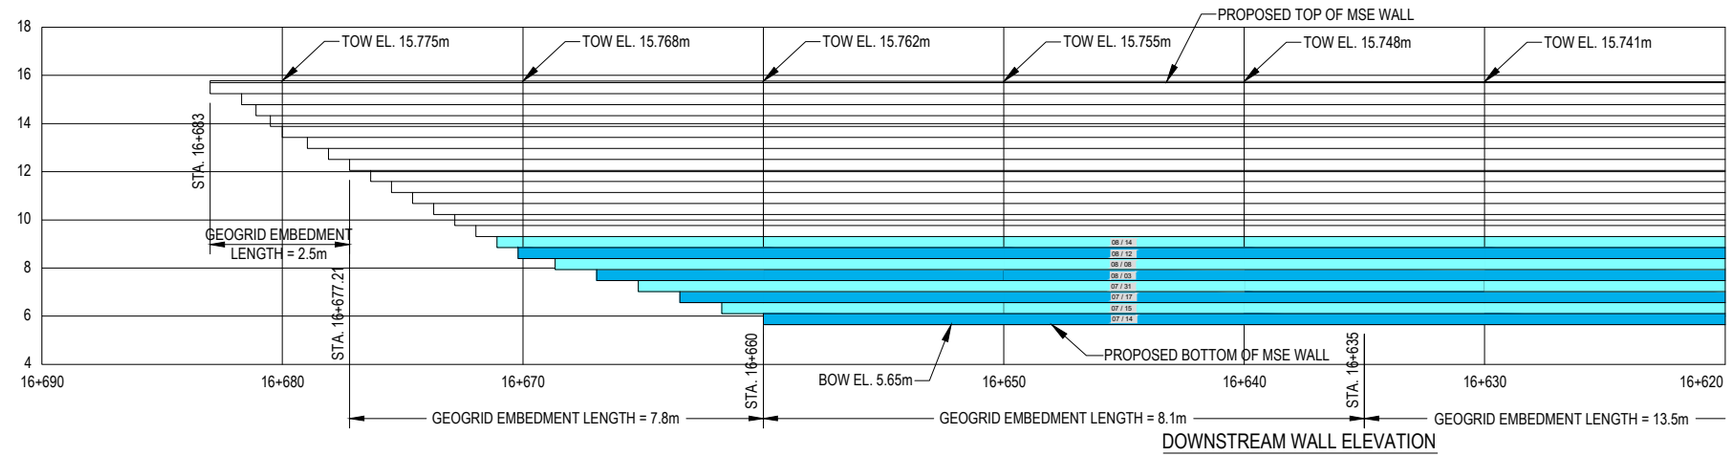

DOWNSTREAM WALL ELEVATION

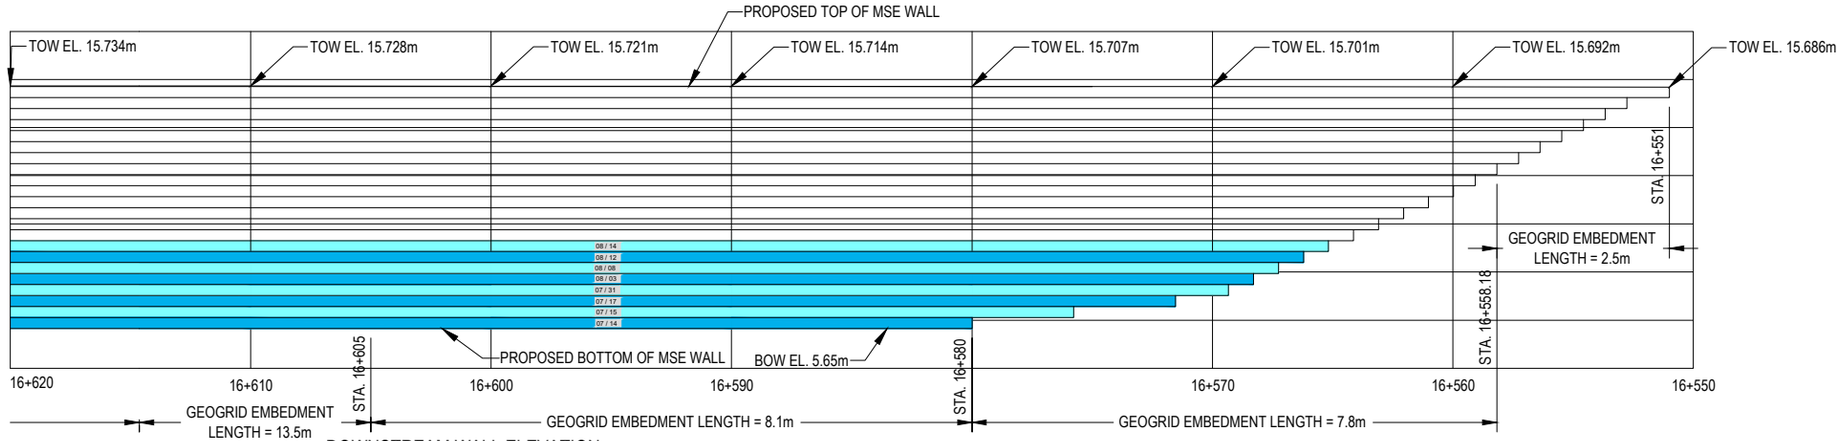

DOWNSTREAM WALL ELEVATION

UPSTREAM WALL ELEVATION

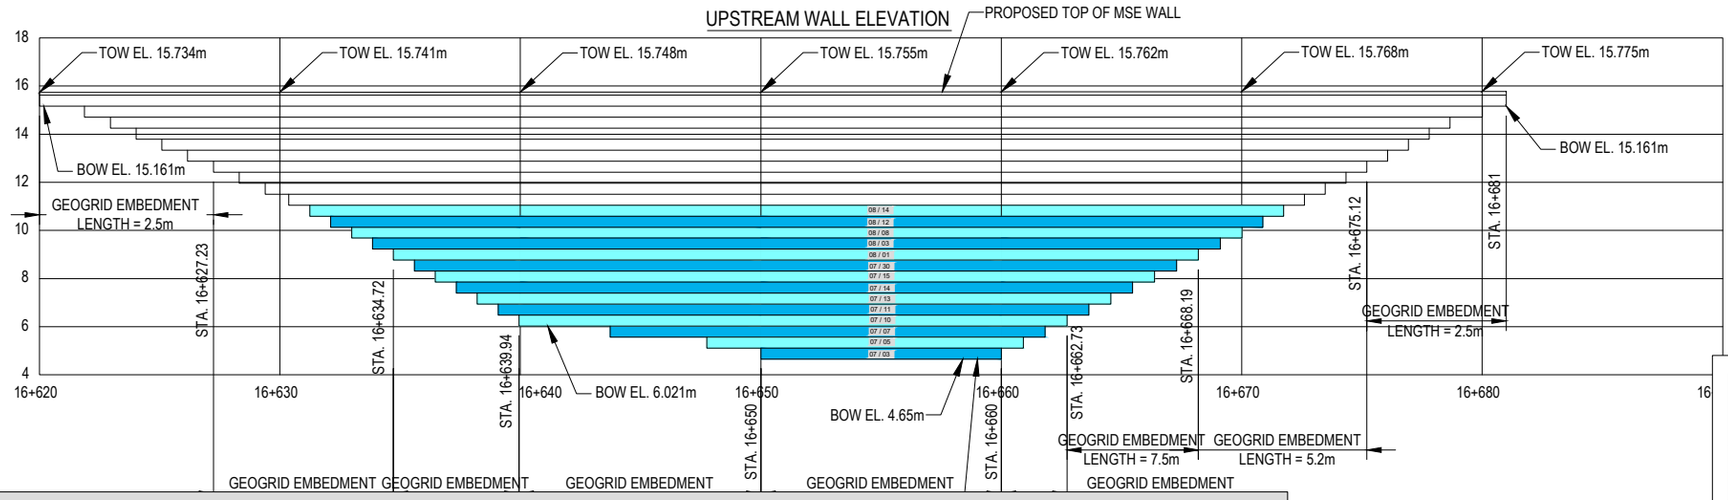

Appendix B - Mechanically Stabilized Earth Walls Structure C

PRINCE RUPERT Port Authority
CANADA'S LEADING PORT
200 – 215 Cow Bay Road
PRINCE RUPERT, B.C. V8J 1A2
PHONE: (250) 627-8899
FAX: (250) 627-8980

PROJECT: Ridley Island Export and Logistics Platform

DRAWING TITLE: Structure C Construction Progress

PROJECT NUMBER:	DRAWING NUMBER:	
DATE: 02/07/2025	SCALE: 1:1500	PAPER:
DRAWN: CC	CHECKED: CG	CAD FILE: Structure C – Mechanically Stabilized Earth Wall – Progression Drawing

REV.	BY:	APR:	DATE:	DESCRIPTION:

Last Saved: 1/6/2025 11:11 PM

S:\Volume4\Client Data and Work Design\MSE\ Field Reports\Appendix B – Structure C MSE Walls\MSE\ Structure C Drawings\Structure C – Mechanically Stabilized Earth Wall – Progression Drawing.dwg